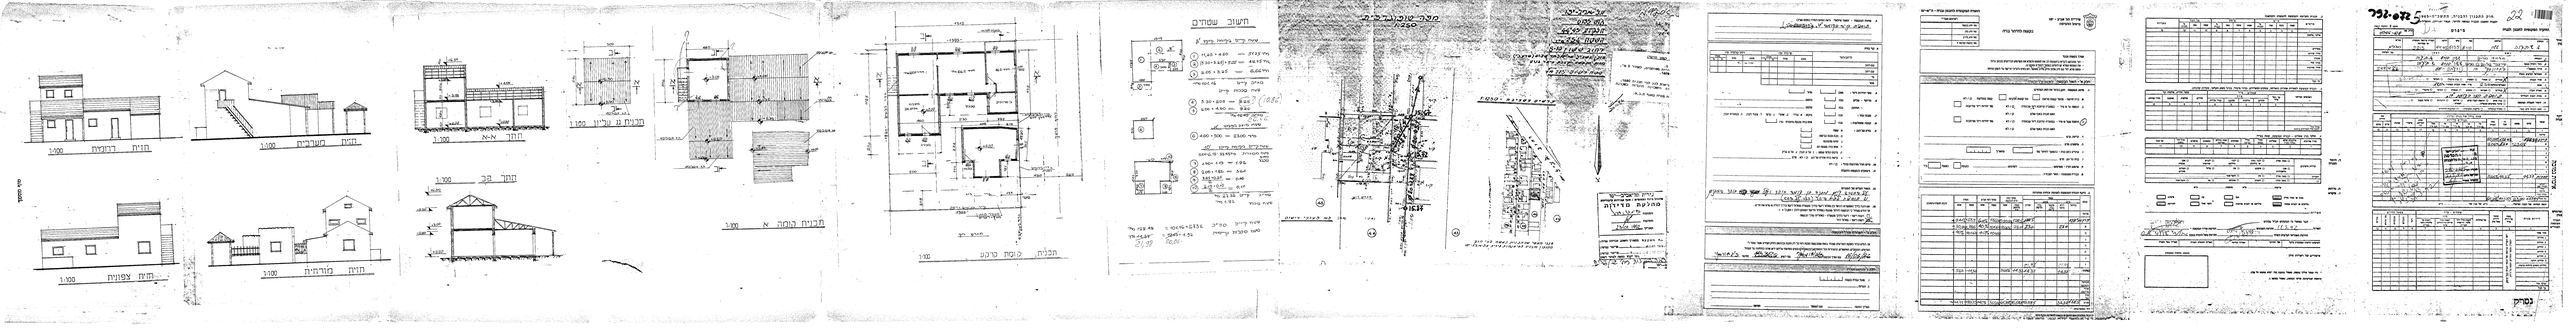
חזית דרומית
1:100
חזית מערבית
1:100
חזית מזרחית
1:100
חזית צפונית
1:100
חתך א-א
1:100
חתך ב-ב
1:100
תכנית גג עליון
1:100
תכנית קומת א
1:100
תכנית קומת קרקע
1:100
חשוב שמדים
מרכז קהילתי רמת-גן
מרכז קהילתי רמת-גן
מרכז קהילתי רמת-גן