מרחב תכנון מקומי תל אביב-יפו
תשריט לתכנית מתאר מס' מק/2751
"שוק התקווה"
בסמכות הועדה המקומית

שינוי מס' 2 לשנת 1998 של תכנית מתאר 2215

מחוז: תל אביב
נפה: תל אביב - יפו
עיר: תל אביב - יפו

תחולת התכנית:
גוש 6979 חלקי חלקות: 3,9-10
גוש 6135 חלקות: 92, 85-89, חלקי חלקות: 68, 53, 49-51

שטח התכנית: כ-27 ד'

היזם:
הועדה המקומית לתכנון ובניה ת"א-יפו

בעל הקרקע:
עיריית ת"א-יפו, חלמיש ופרטיים

המתכנן:
צ. תכנון מזרח, המחלקה לתכנון שוטף,
אגף תב"ע, מנהל ההנדסה עיריית ת"א-יפו

השרטוט הוכן על בסיס מפה מדידה עדכנית
מתאריך 00.00.00 שם ..... חתימה: .....

חתימת המתכנן | חתימת הרשם (מהנדס הועדה) | חתימת בעל הקרקע

ועדה מקומית תל-אביב-יפו
אישור תכנית מס' מק/2751
הוגשה לוועדה המקומית לאישור ע"פ סעיף 106(ב)
בישיבתה מס' 2-23 מיום 2.6.99
יו"ר הוועדה המקומית

הועדה המקומית לתכנון ובניה
התכנית מאושרת
בהתאם לסעיף 106 (ב)
לחוק התכנון והבניה
תשכ"ה-1965
חתימת בעל הקרקע

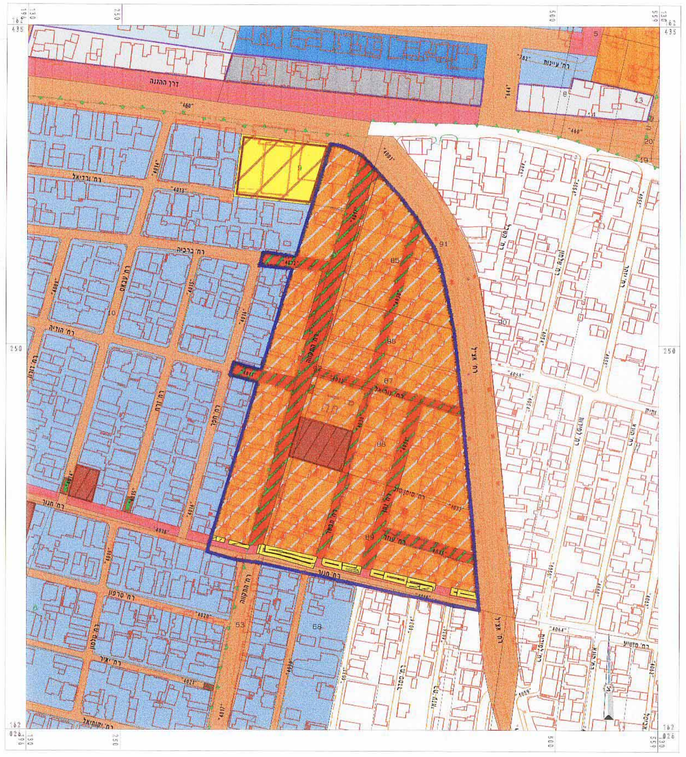

תכנית מצב קיים קנ"מ 1:1250

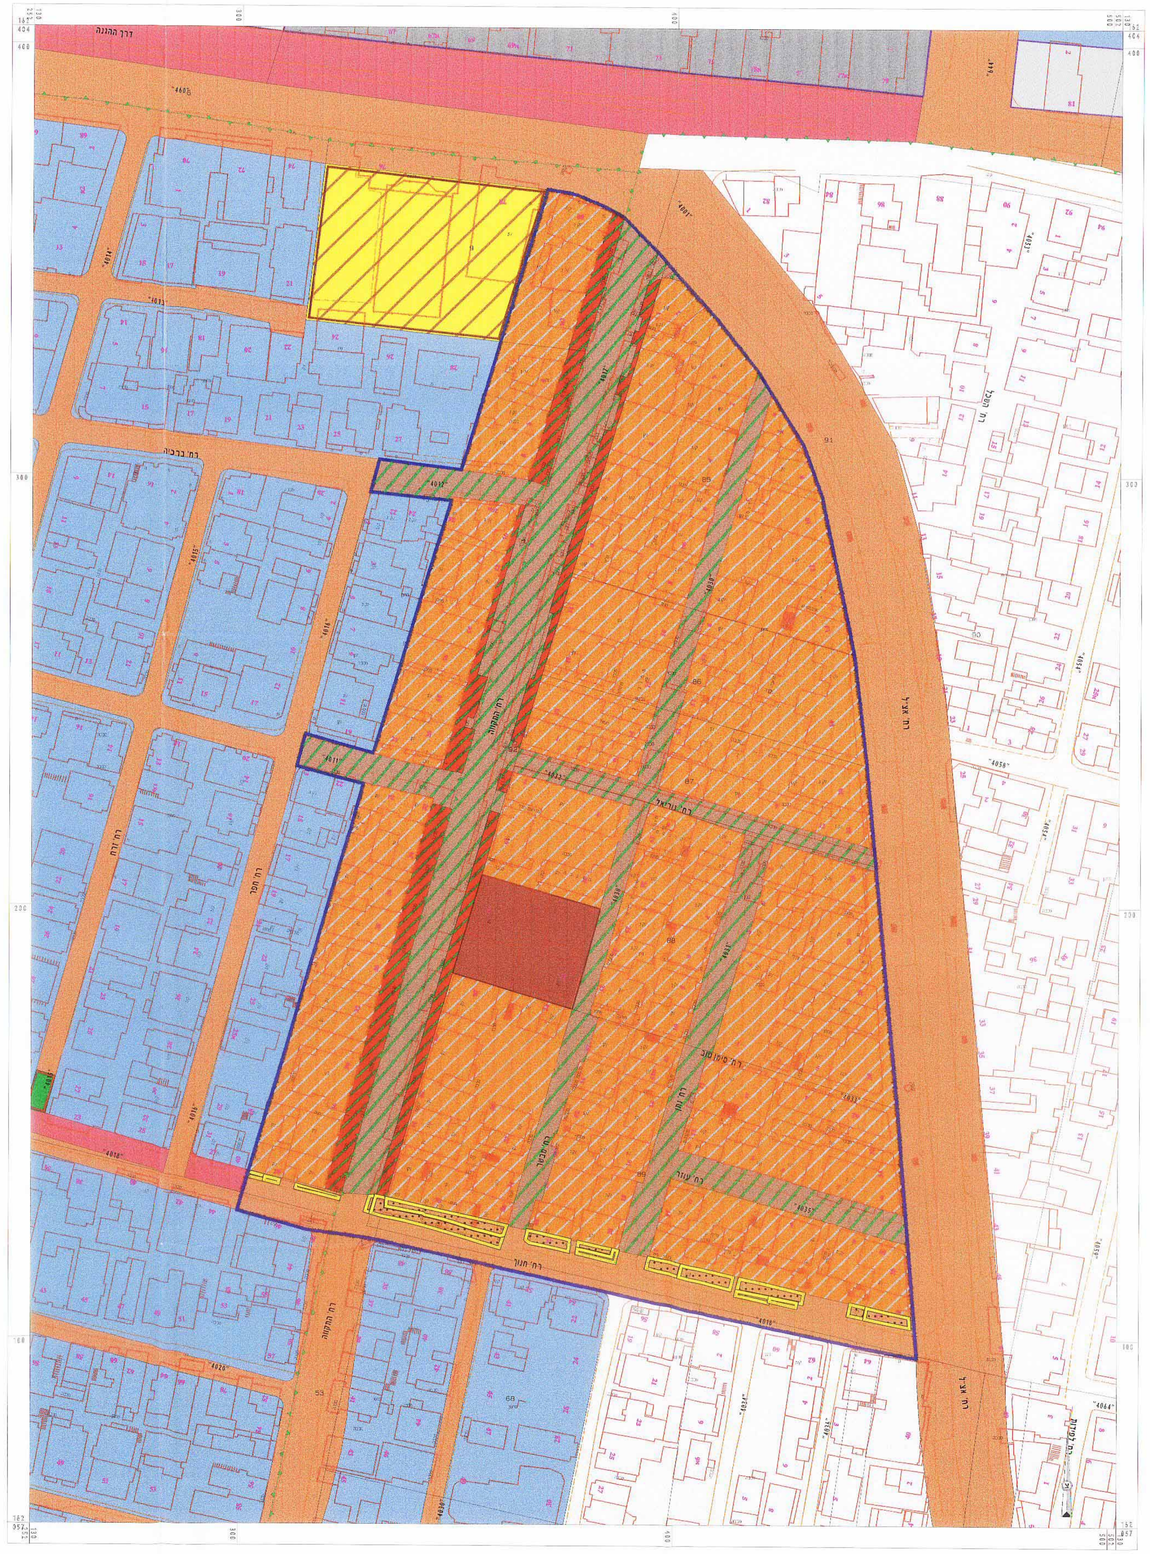

תכנית מצב מוצע קנ"מ 1:500

מקרא מצב קיים

- גבול תכנית
- גבול גוש
- גבול חלקה קיימת
- גבול תכנית תקפה
- דרך קיימת
- דרך מוצעת
- אזור מסחרי מגורים
- בניני ציבור מוצע
- דרך משולבת מוצעת
- בנין להריסה

יעודים שאינם כלולים בשטח התוכנית

- אזור מגורים א
- מגורים ב'
- שביל להולכי רגל
- אזור מסחרי
- מגורים 2 קומות
- מגרש מיוחד
- מסחרי א'
- מגורים א'2
- כללי

מקרא מצב מוצע

- גבול תכנית
- גבול גוש
- גבול חלקה קיימת
- גבול מגרש מוצע
- דרך קיימת
- בנייני ציבור
- אזור מסחרי מגורים
- דרך משולבת קיימת
- דרך משולבת מוצעת
- בנין להריסה

יעודים שאינם כלולים בשטח התוכנית

- דרך מוצעת
- מגורים ב'
- שביל להולכי רגל
- אזור מסחרי
- מגרש מיוחד
- מסחרי א'
- כללי

טבלת שטחים מצב קיים

יעוד	שטח יעוד	% מהשטח
דרך קיימת	1558	5.8
בנייני ציבור	495	1.8
אזור מסחרי מגורים	18174	67.4
דרך משולבת קיימת	5134	19.0
דרך משולבת מוצעת	1640	6.0
סה"כ שטח:	26949	

טבלת שטחים מצב מוצע

יעוד	שטח יעוד	% מהשטח
דרך קיימת	762	2.8
דרך מוצעת	796	3.0
אזור מסחרי מגורים	19469	72.3
בנייני ציבור מוצע	757	2.8
דרך משולבת מוצעת	5234	19.4
סה"כ שטח:	26949	

מדבר ראיר למידע הנדסי