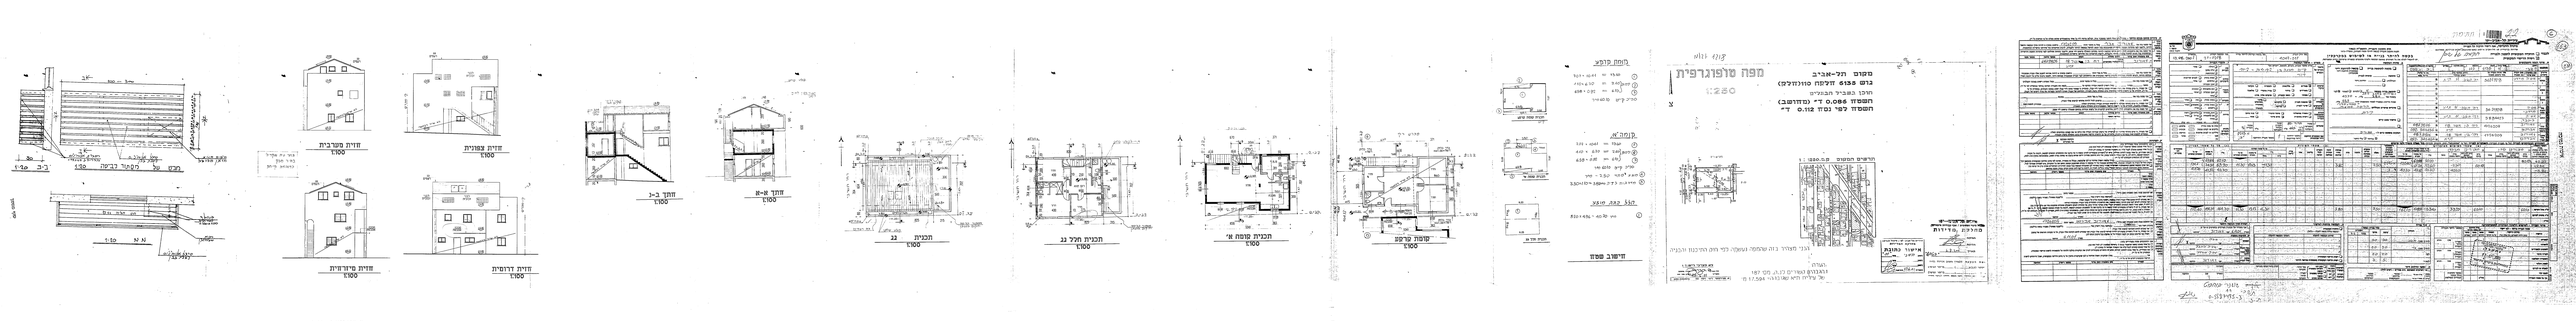
מפה טופוגרפית
1:250
מקום תל-אביב
גוש 6123 חלקה מוחלט(כל)
רחוב כאבוך הבנים
השטח 0.086 ד' (מחושב)
השטח לפי נסח 0.12 ד'
חזית מערבית
חזית צפונית
חזית דרומית
חזית מזרחית
חתך א-א
חתך ב-ב
תכנית מצב
תכנית מלא ב
תכנית קומה א'
תכנית גג
חישוב שטח
מרכז מידות
מדידות
מדידה מחדש
מדידה מקורית
מדידה מקורית
מדידה מחדש
מדידה מקורית
מדידה מחדש
מדידה מקורית
מדידה מחדש